


242 × 122 = 1

ضخامت های لبه زائد: 1 ⇐ 1 ⇑ 1 ⇨ 1 ⇓ 1

آقای بابایی / 1 / PVC

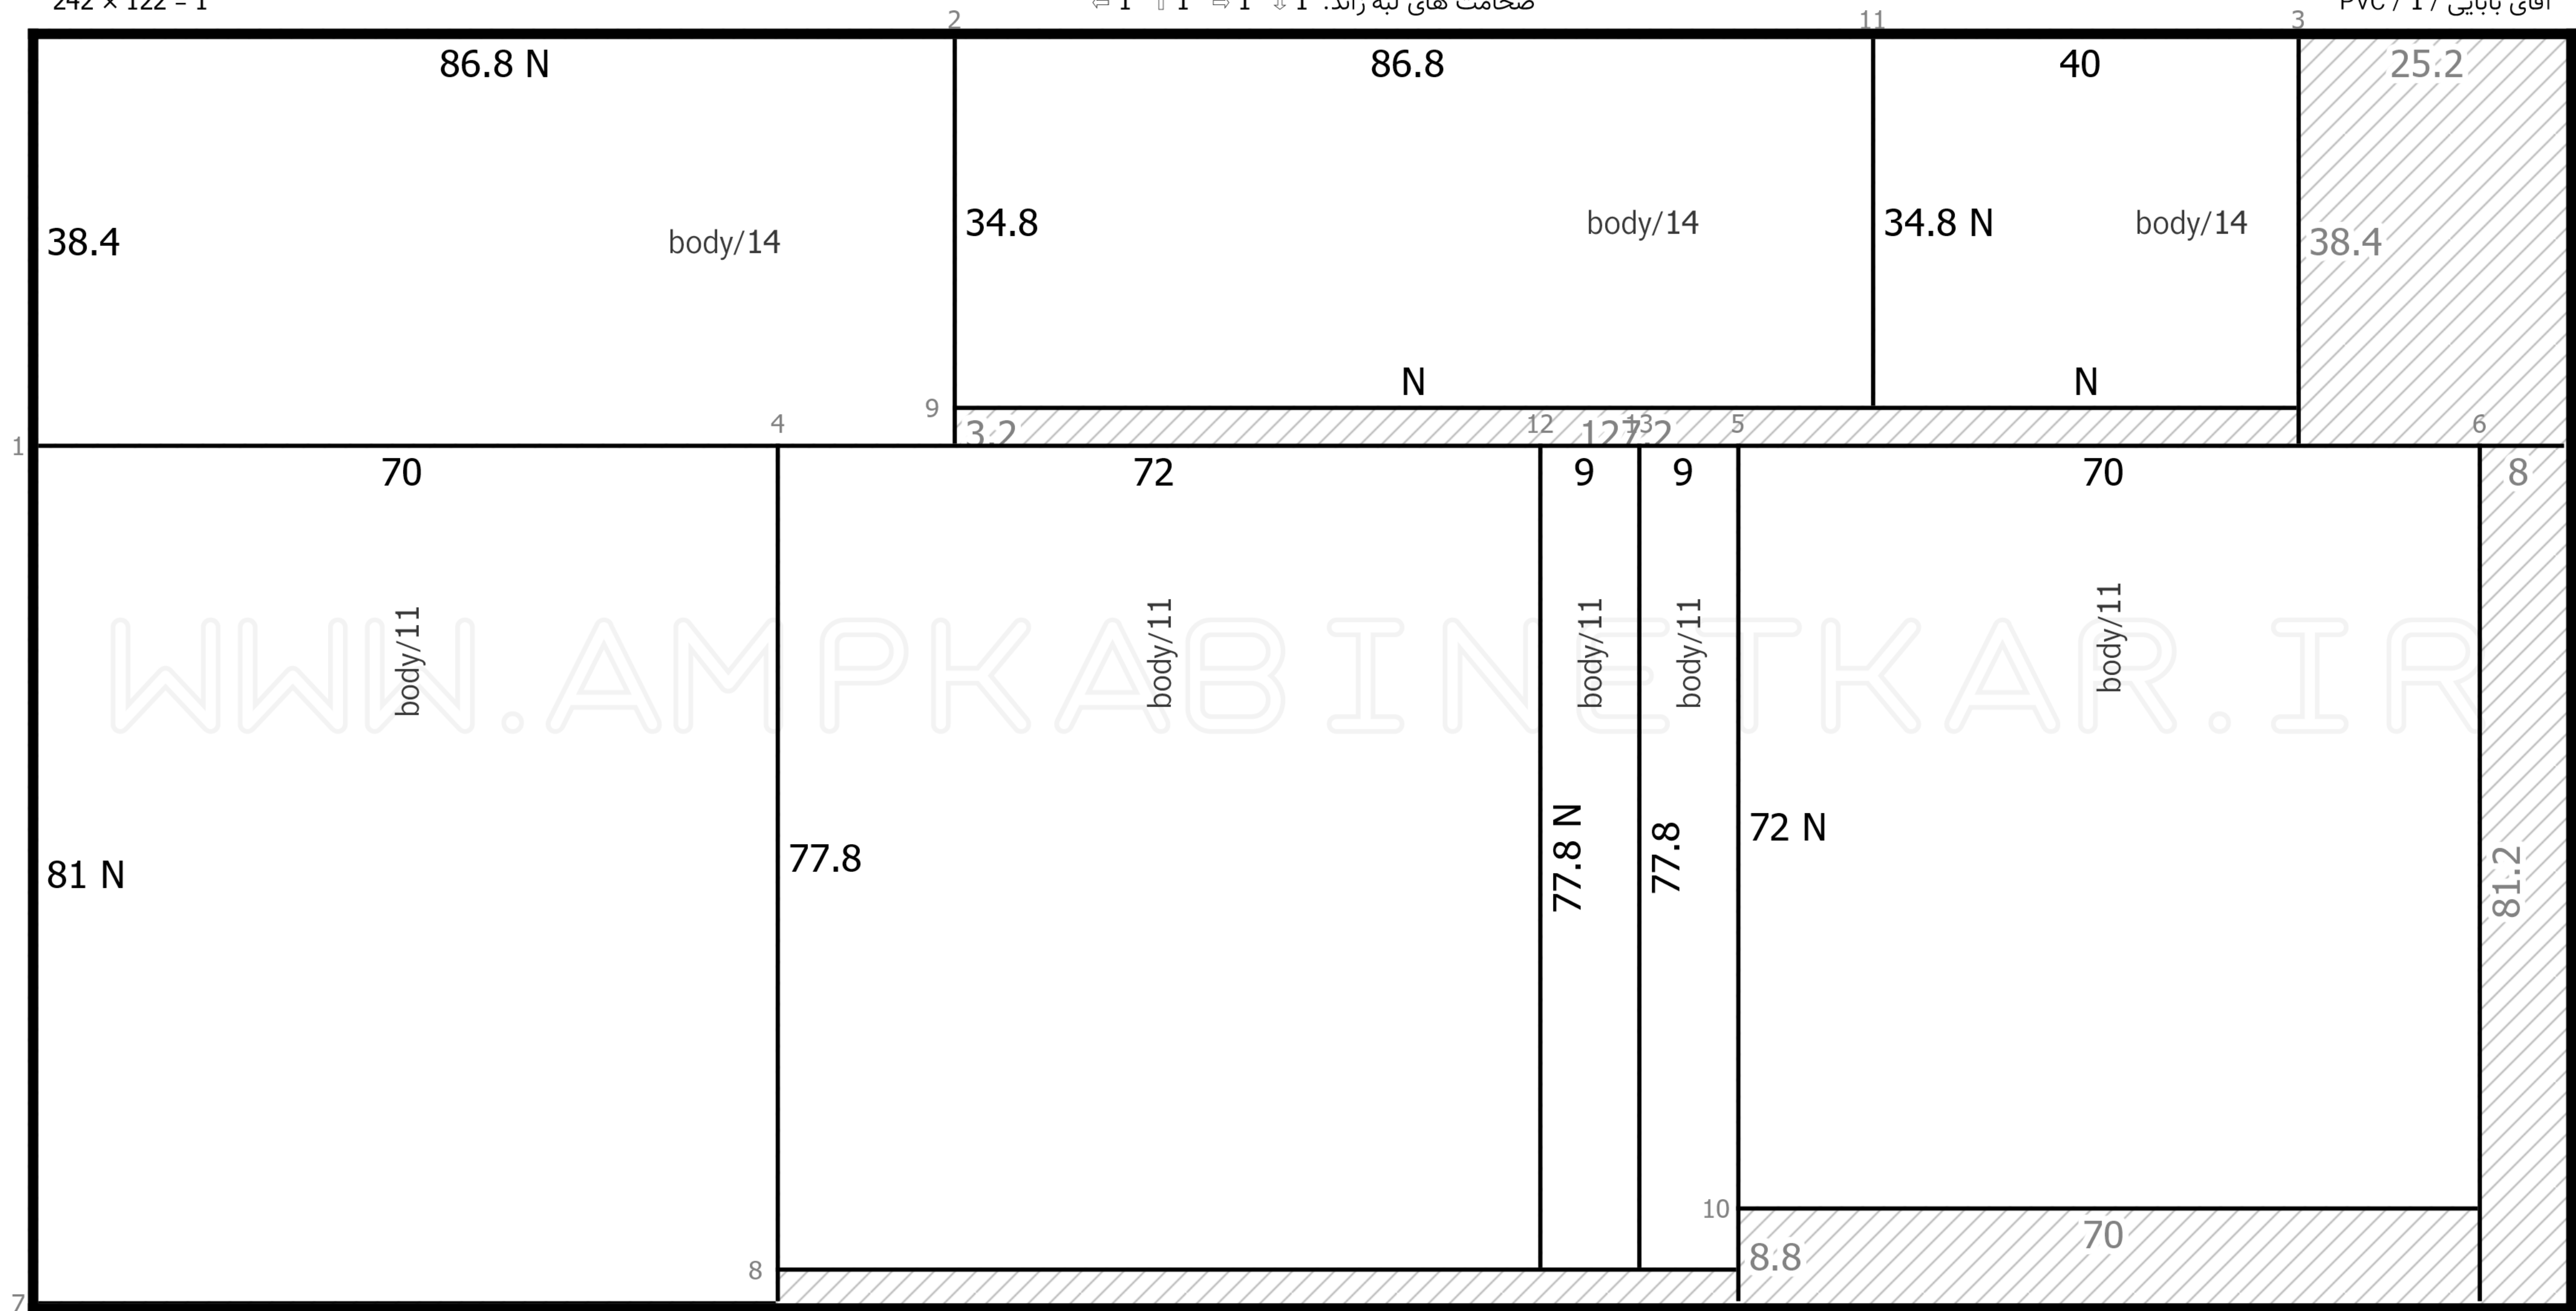

مساحت استفاده شده: 2.55 مترمربع | مساحت باقیمانده: 0.29 مترمربع | تعداد قطعات: 8 | تعداد قطعات اضافه: 5 | تعداد برش: 13 | بهینه سازی: 90.1% | پرتی: 9.9%

