



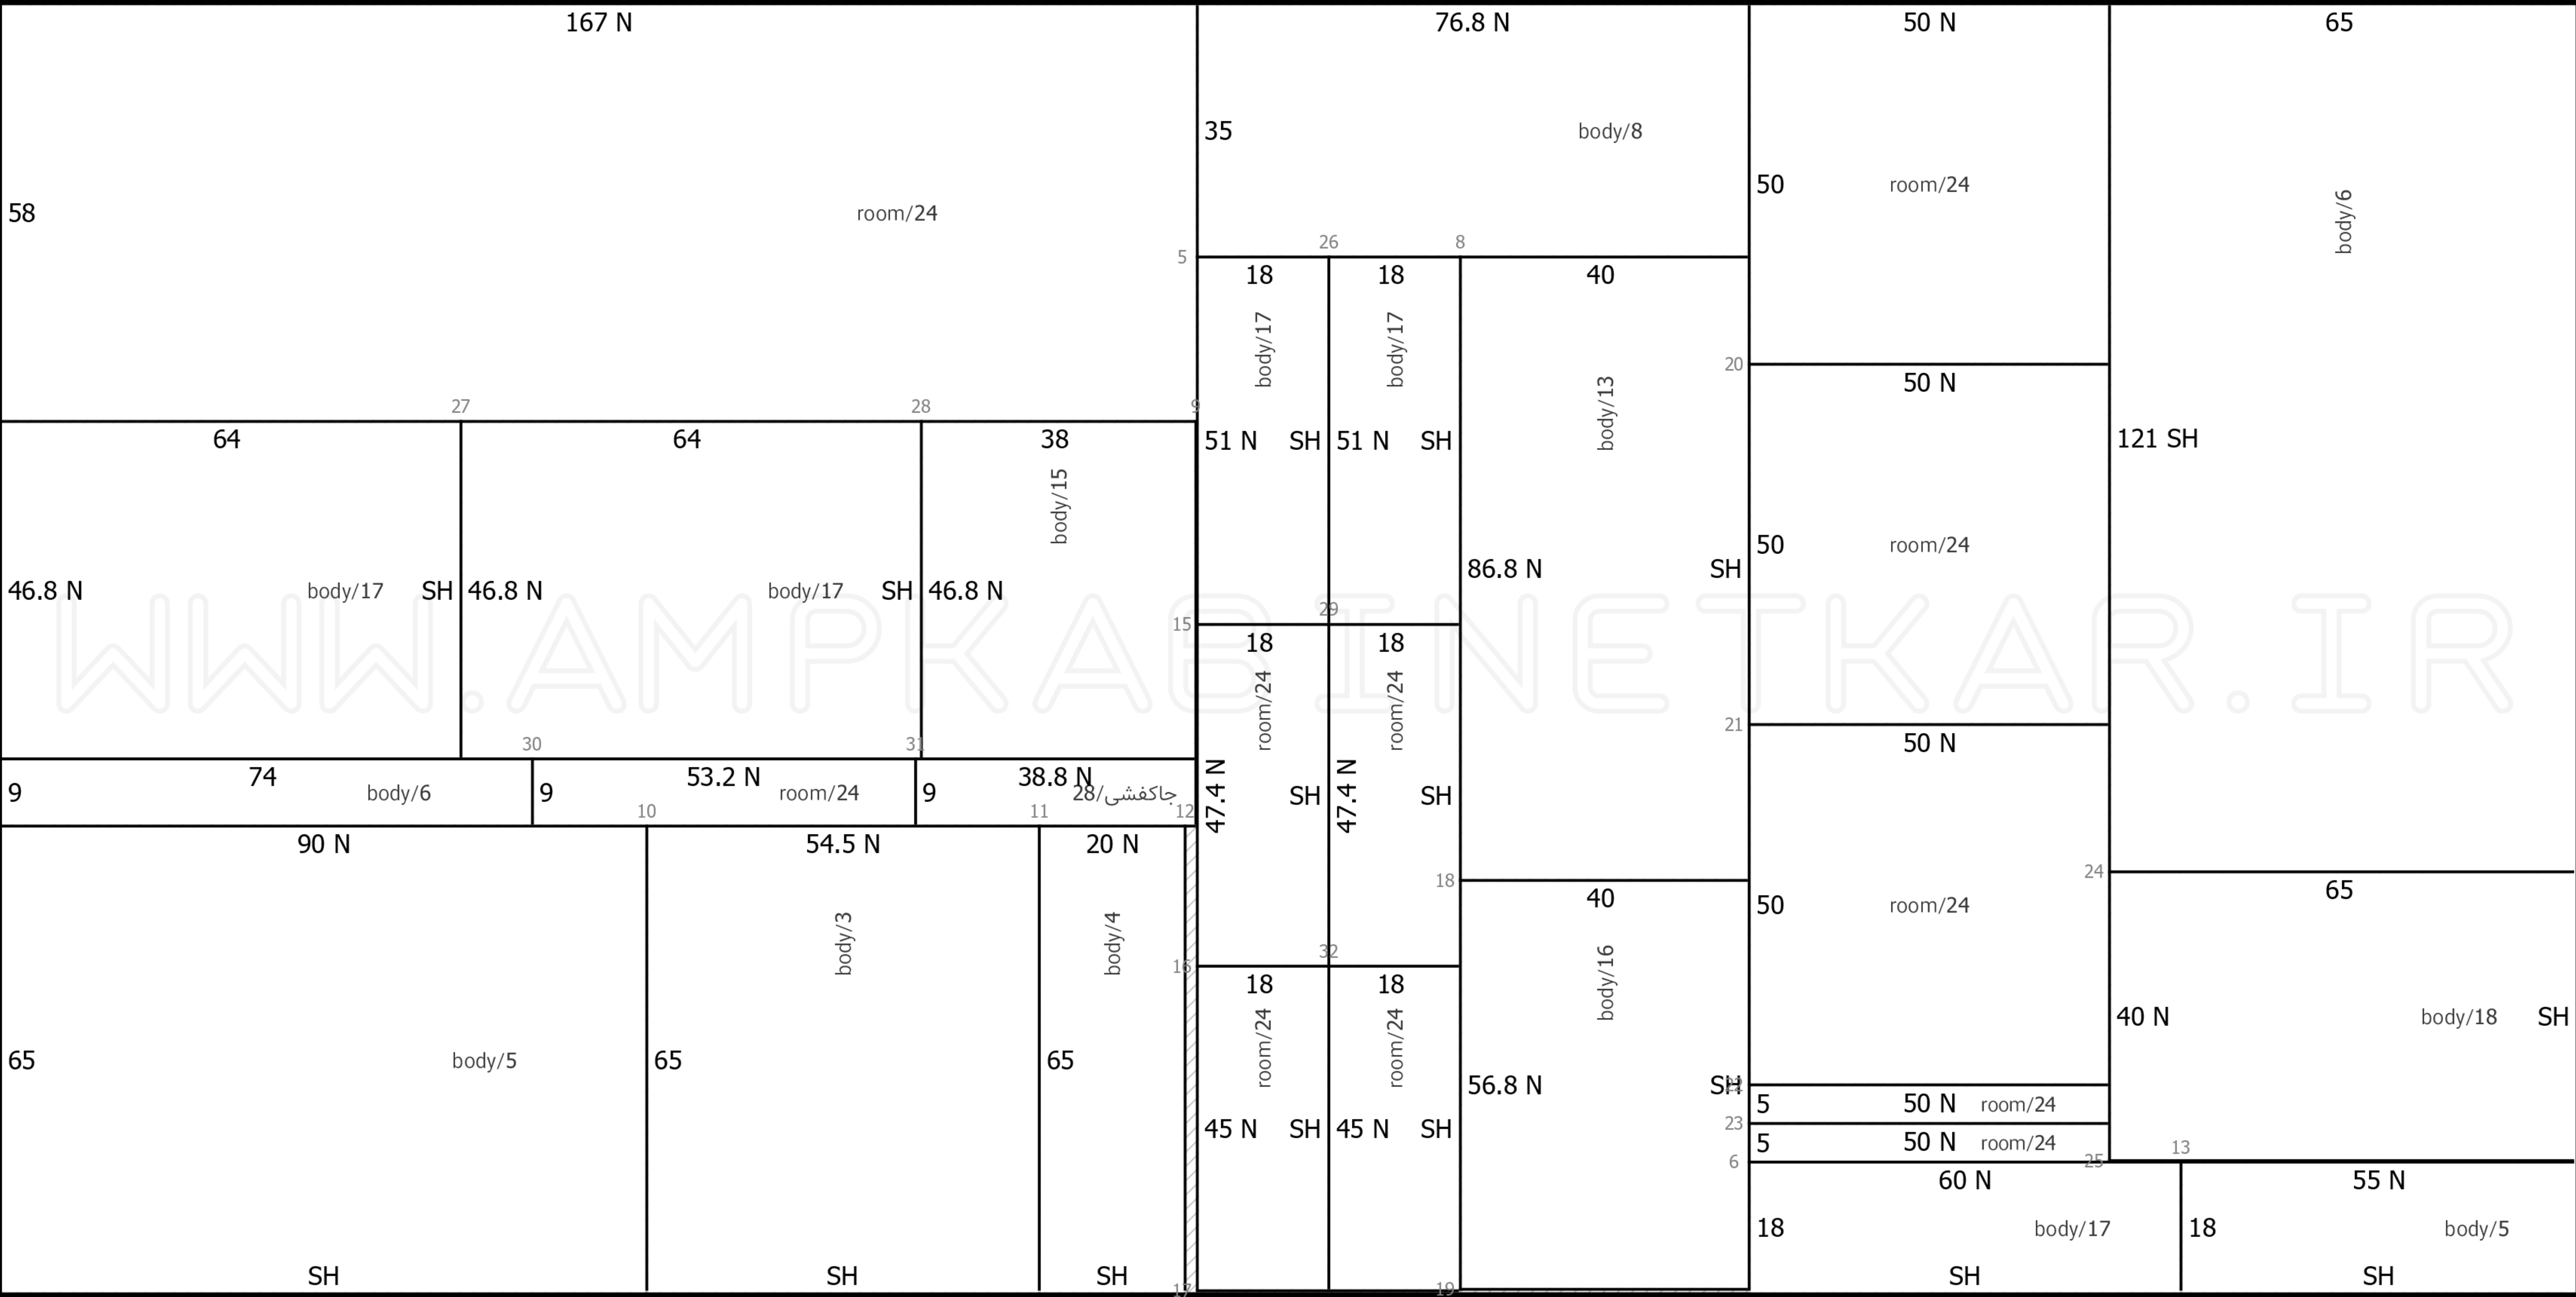


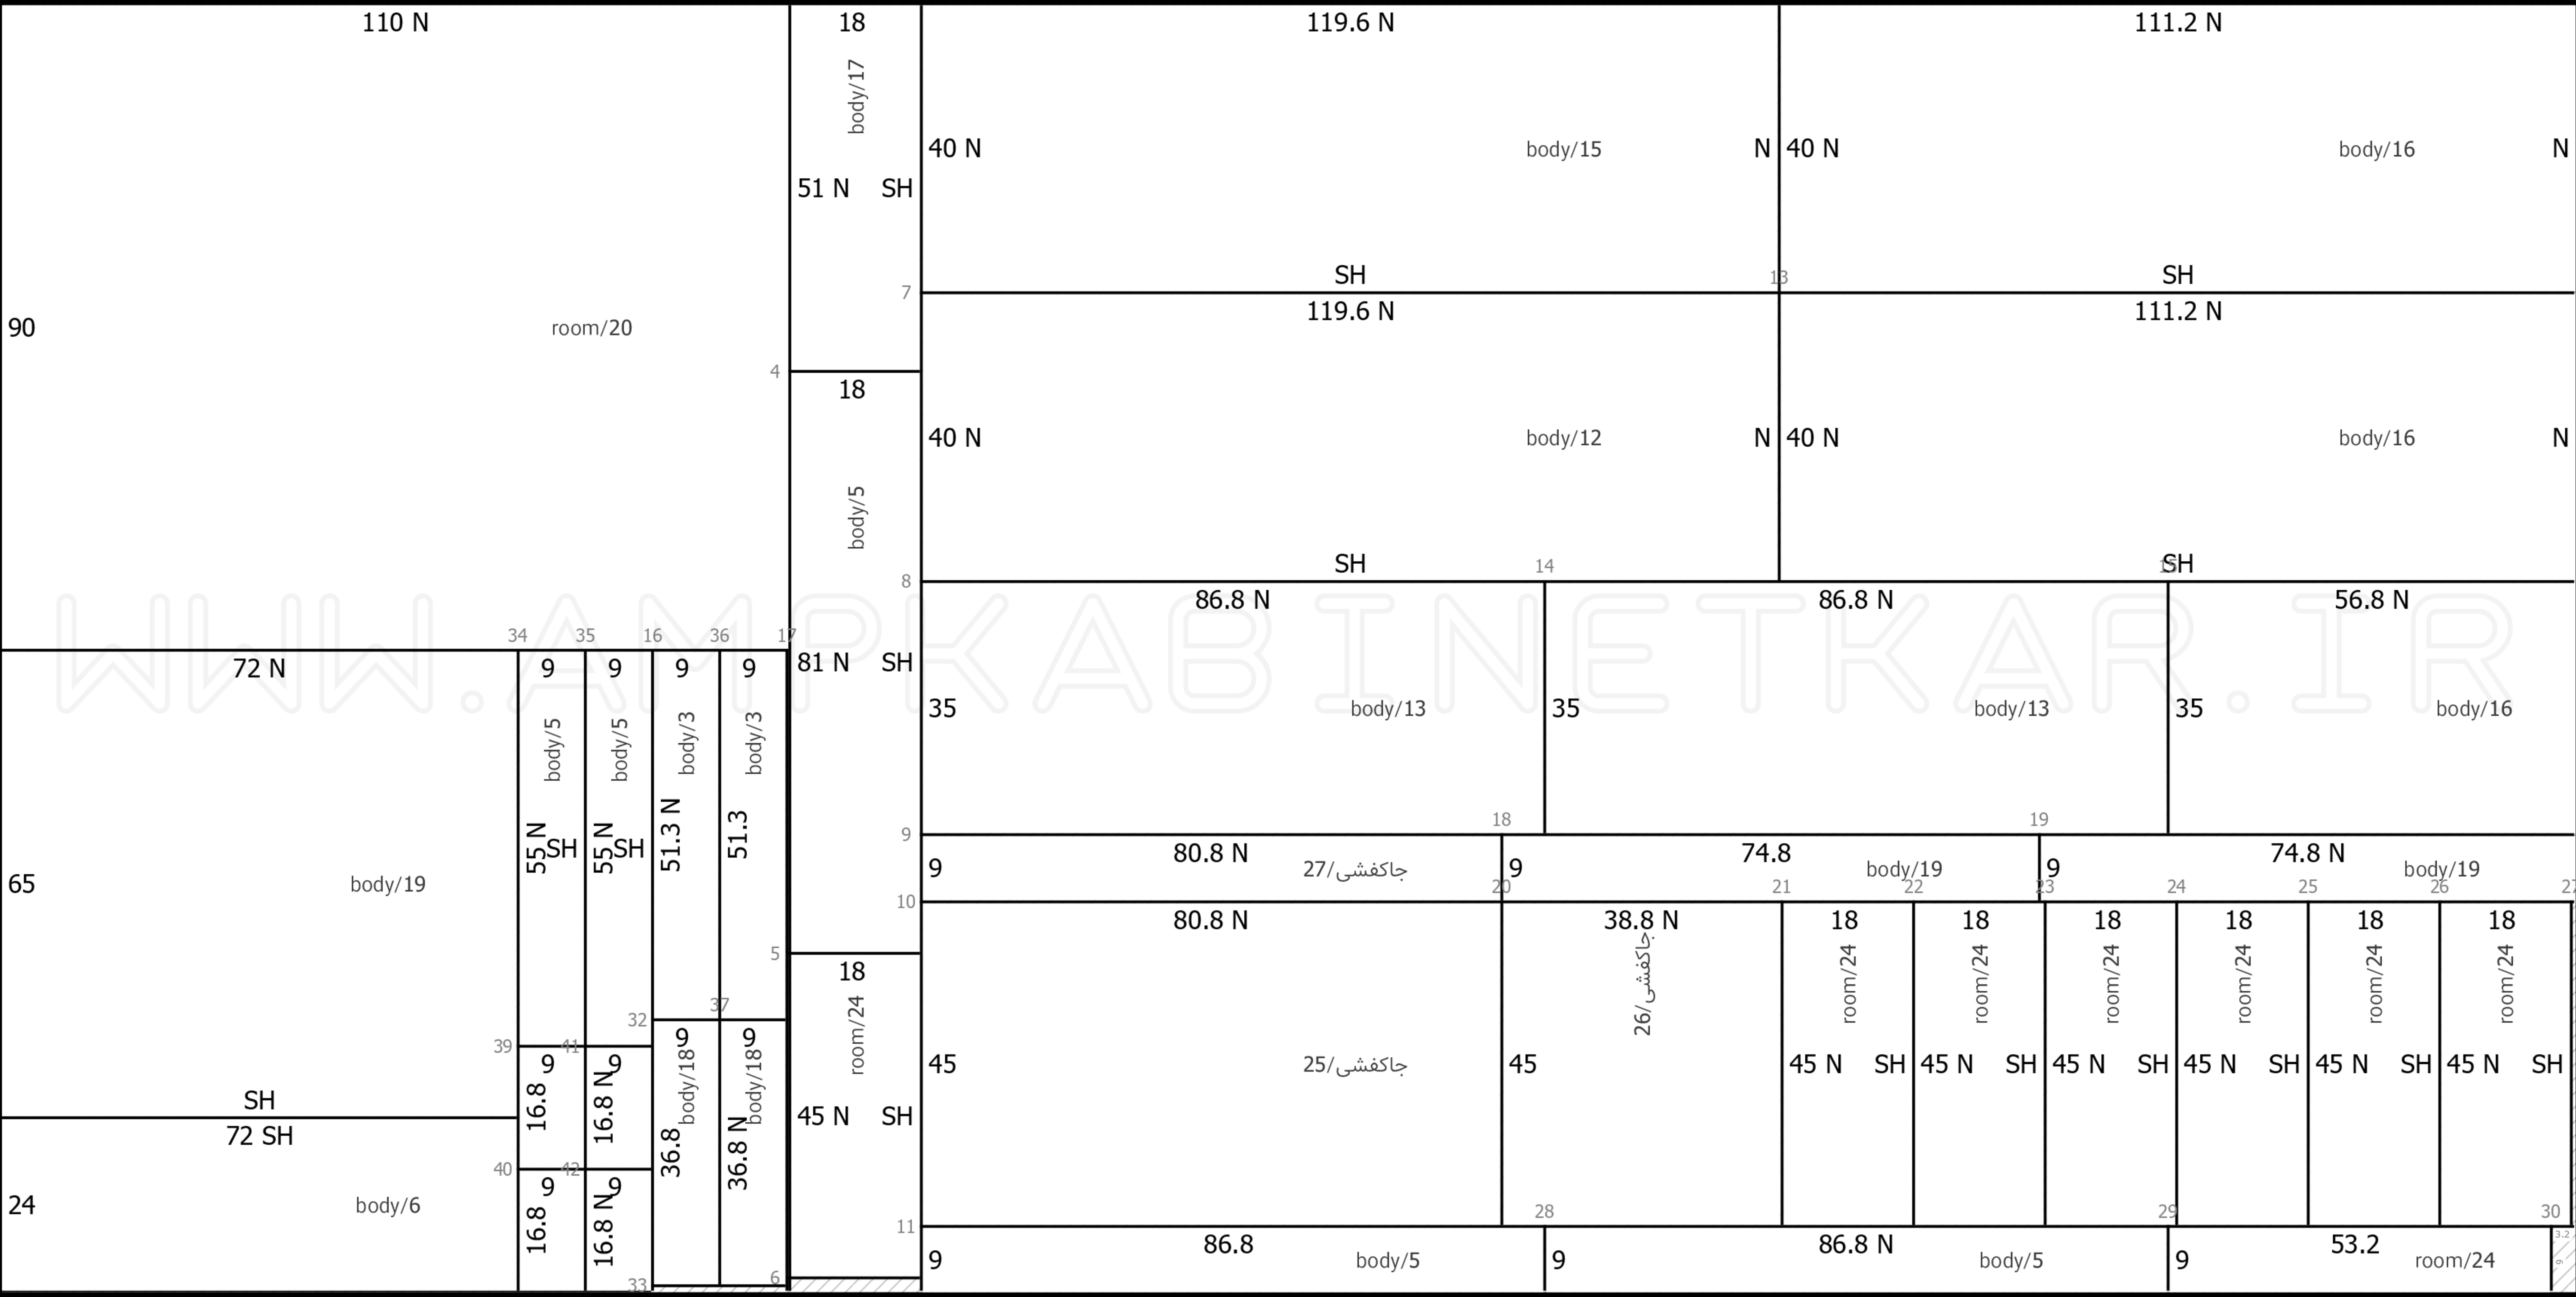

362 × 182 = 1

ضخامت های لبه زائد: 1 ⇐ 1 ⇨ 1 1 ↓

آقای بابایی / بدنه / 3

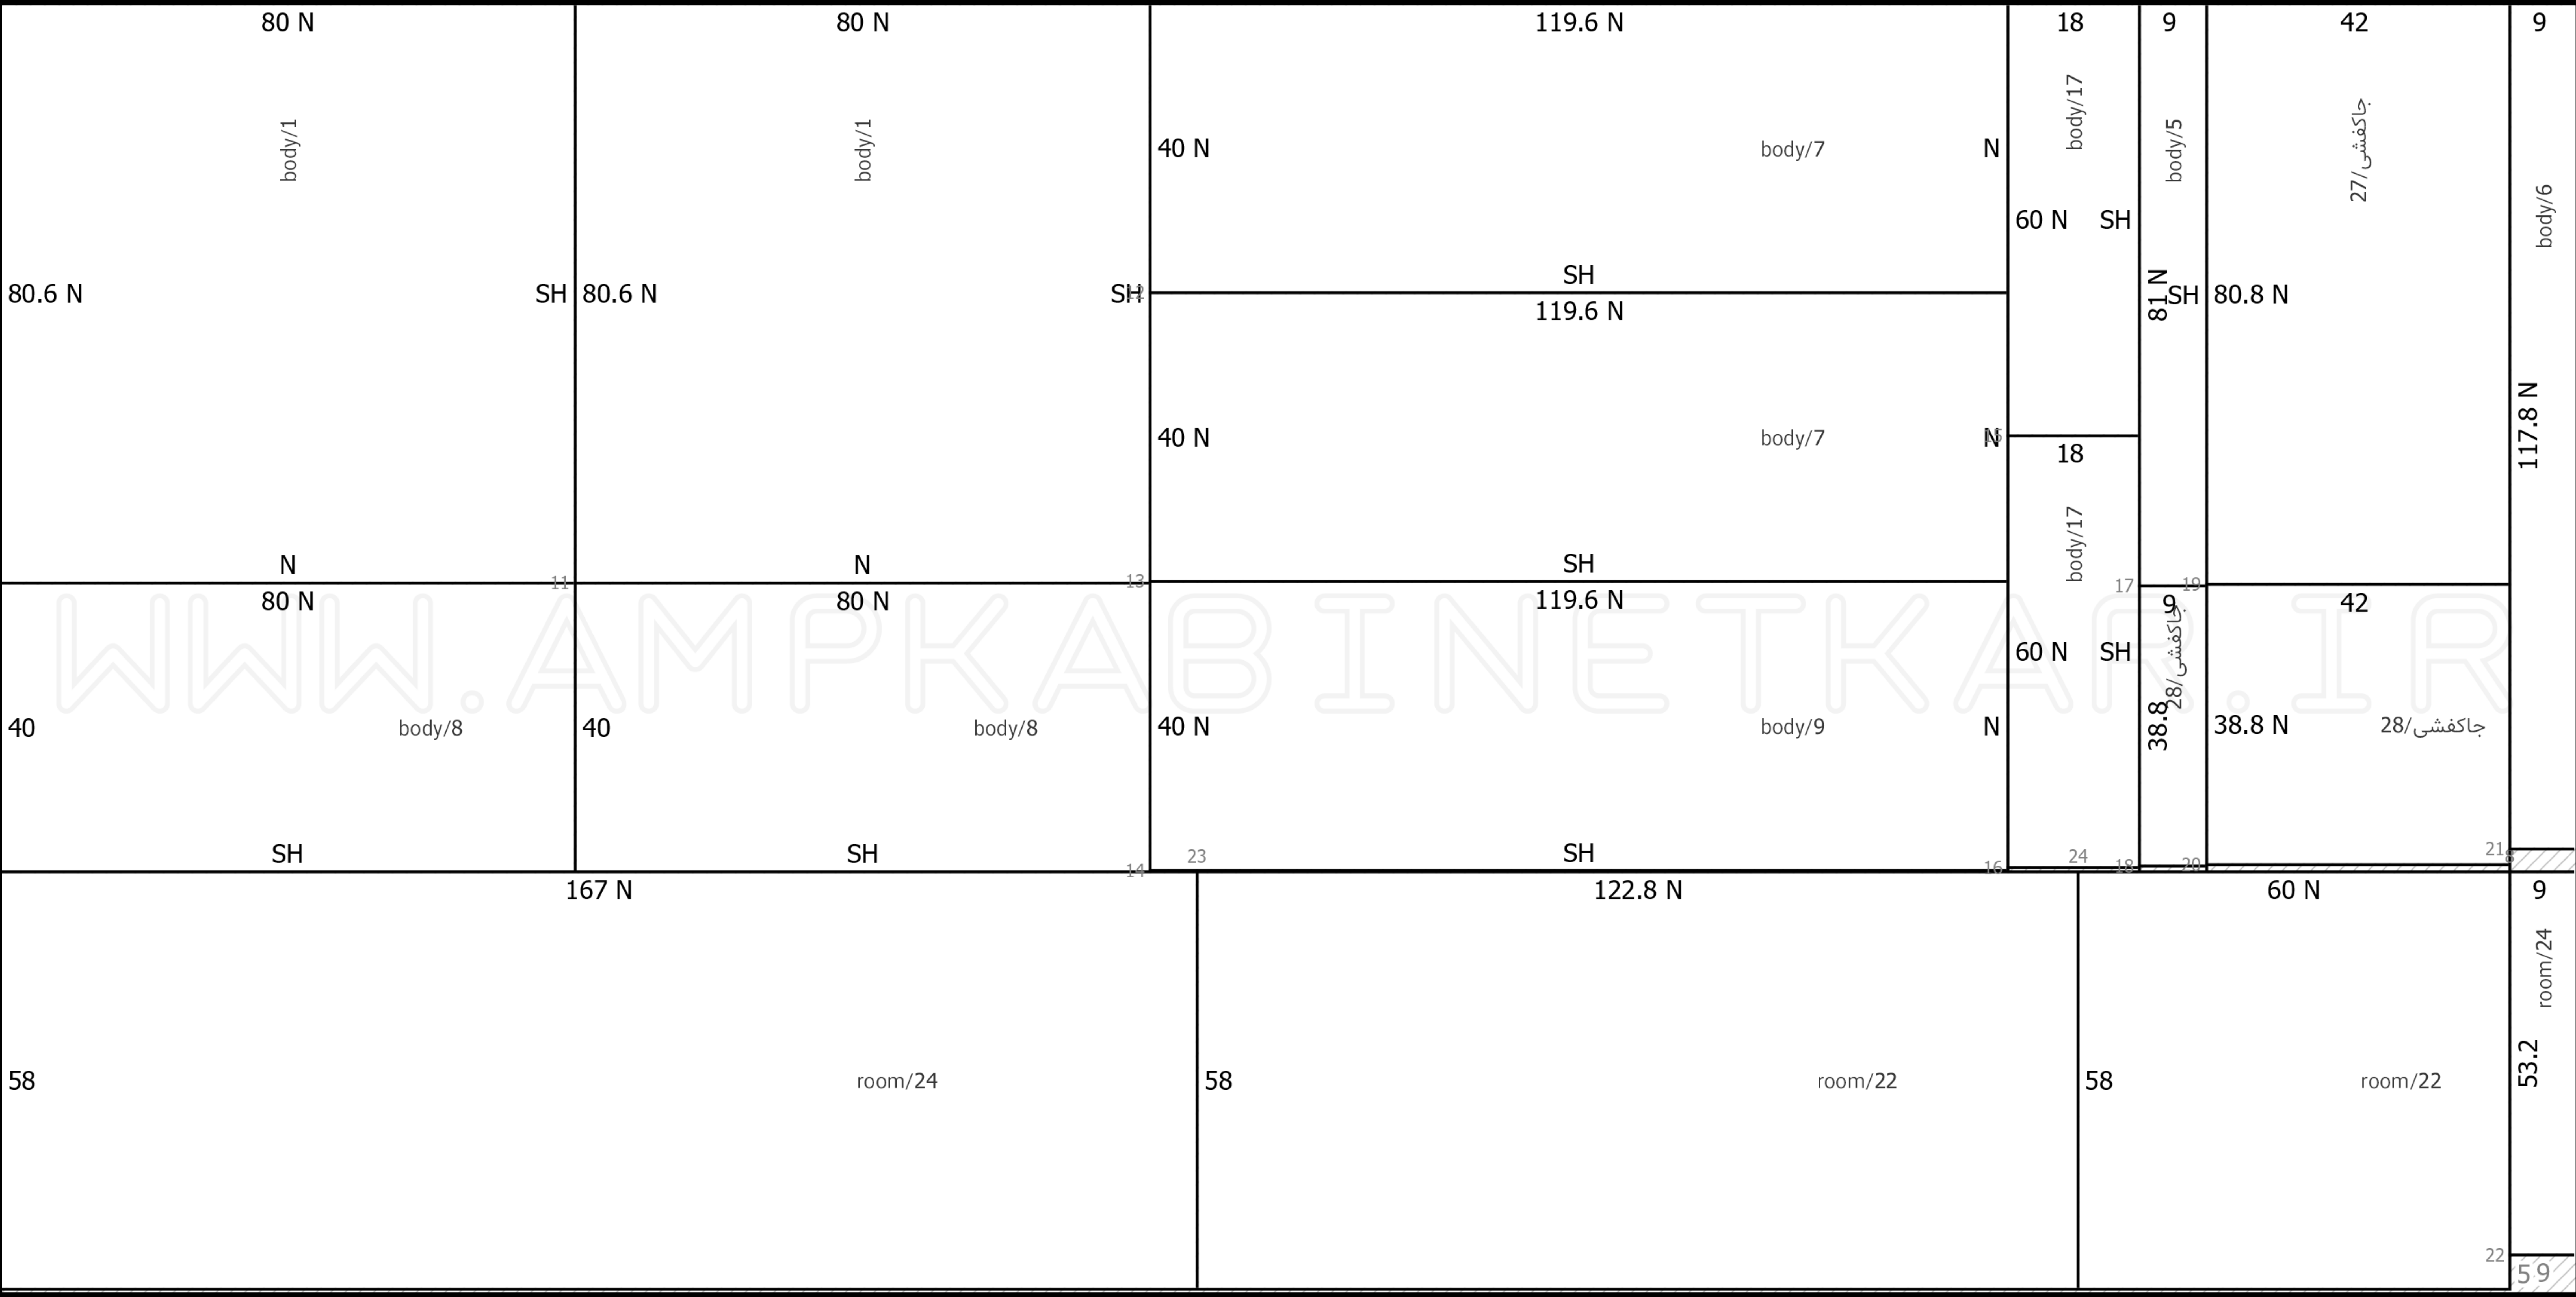


مساحت استفاده شده: 6.37 مترمربع | مساحت باقیمانده: 0.02 مترمربع | تعداد قطعات: 18 | تعداد قطعات اضافه: 6 | تعداد برش: 24 | بهینه سازی: 99.7% | پرتی: 0.3%


362 × 182 = 1

ضخامت های لبه زائد: 1 ↓ 1 ⇒ 1 ↑ 1 ⇐ 1

آقای بابایی / بدنه / 4

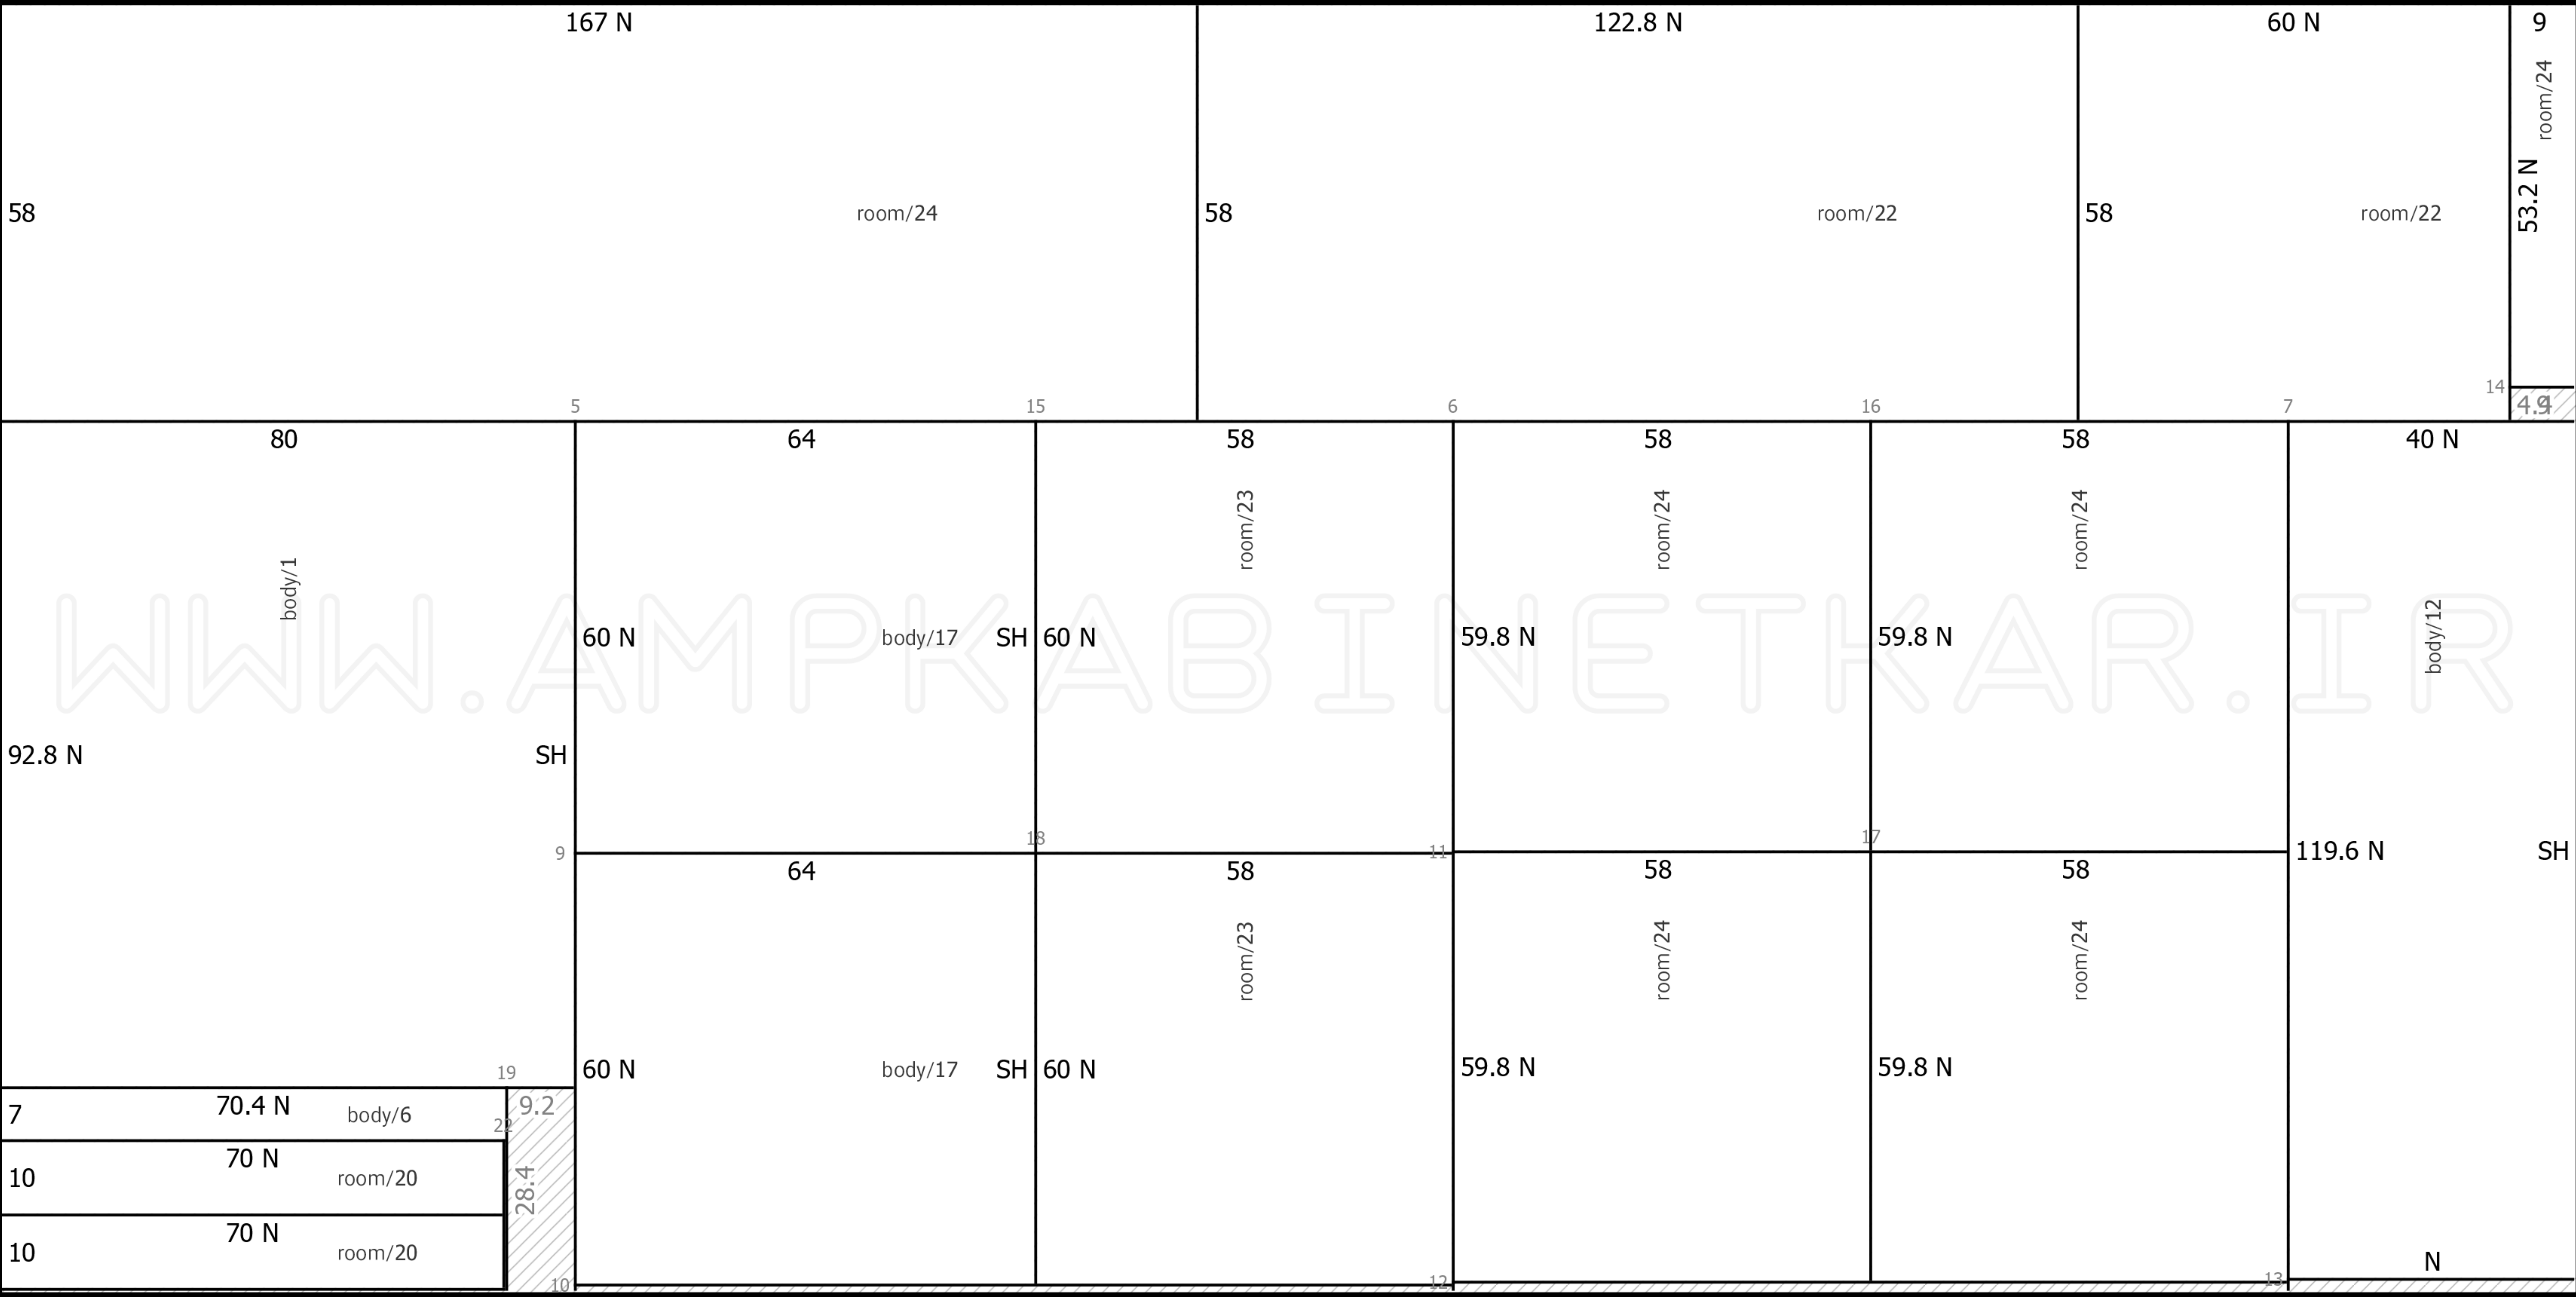


مساحت استفاده شده: 6.34 مترمربع | مساحت باقیمانده: 0.06 مترمربع | تعداد قطعات: 17 | تعداد قطعات اضافه: 6 | تعداد برش: 23 | بهینه سازی: 99.1% | پرتی: 0.9%

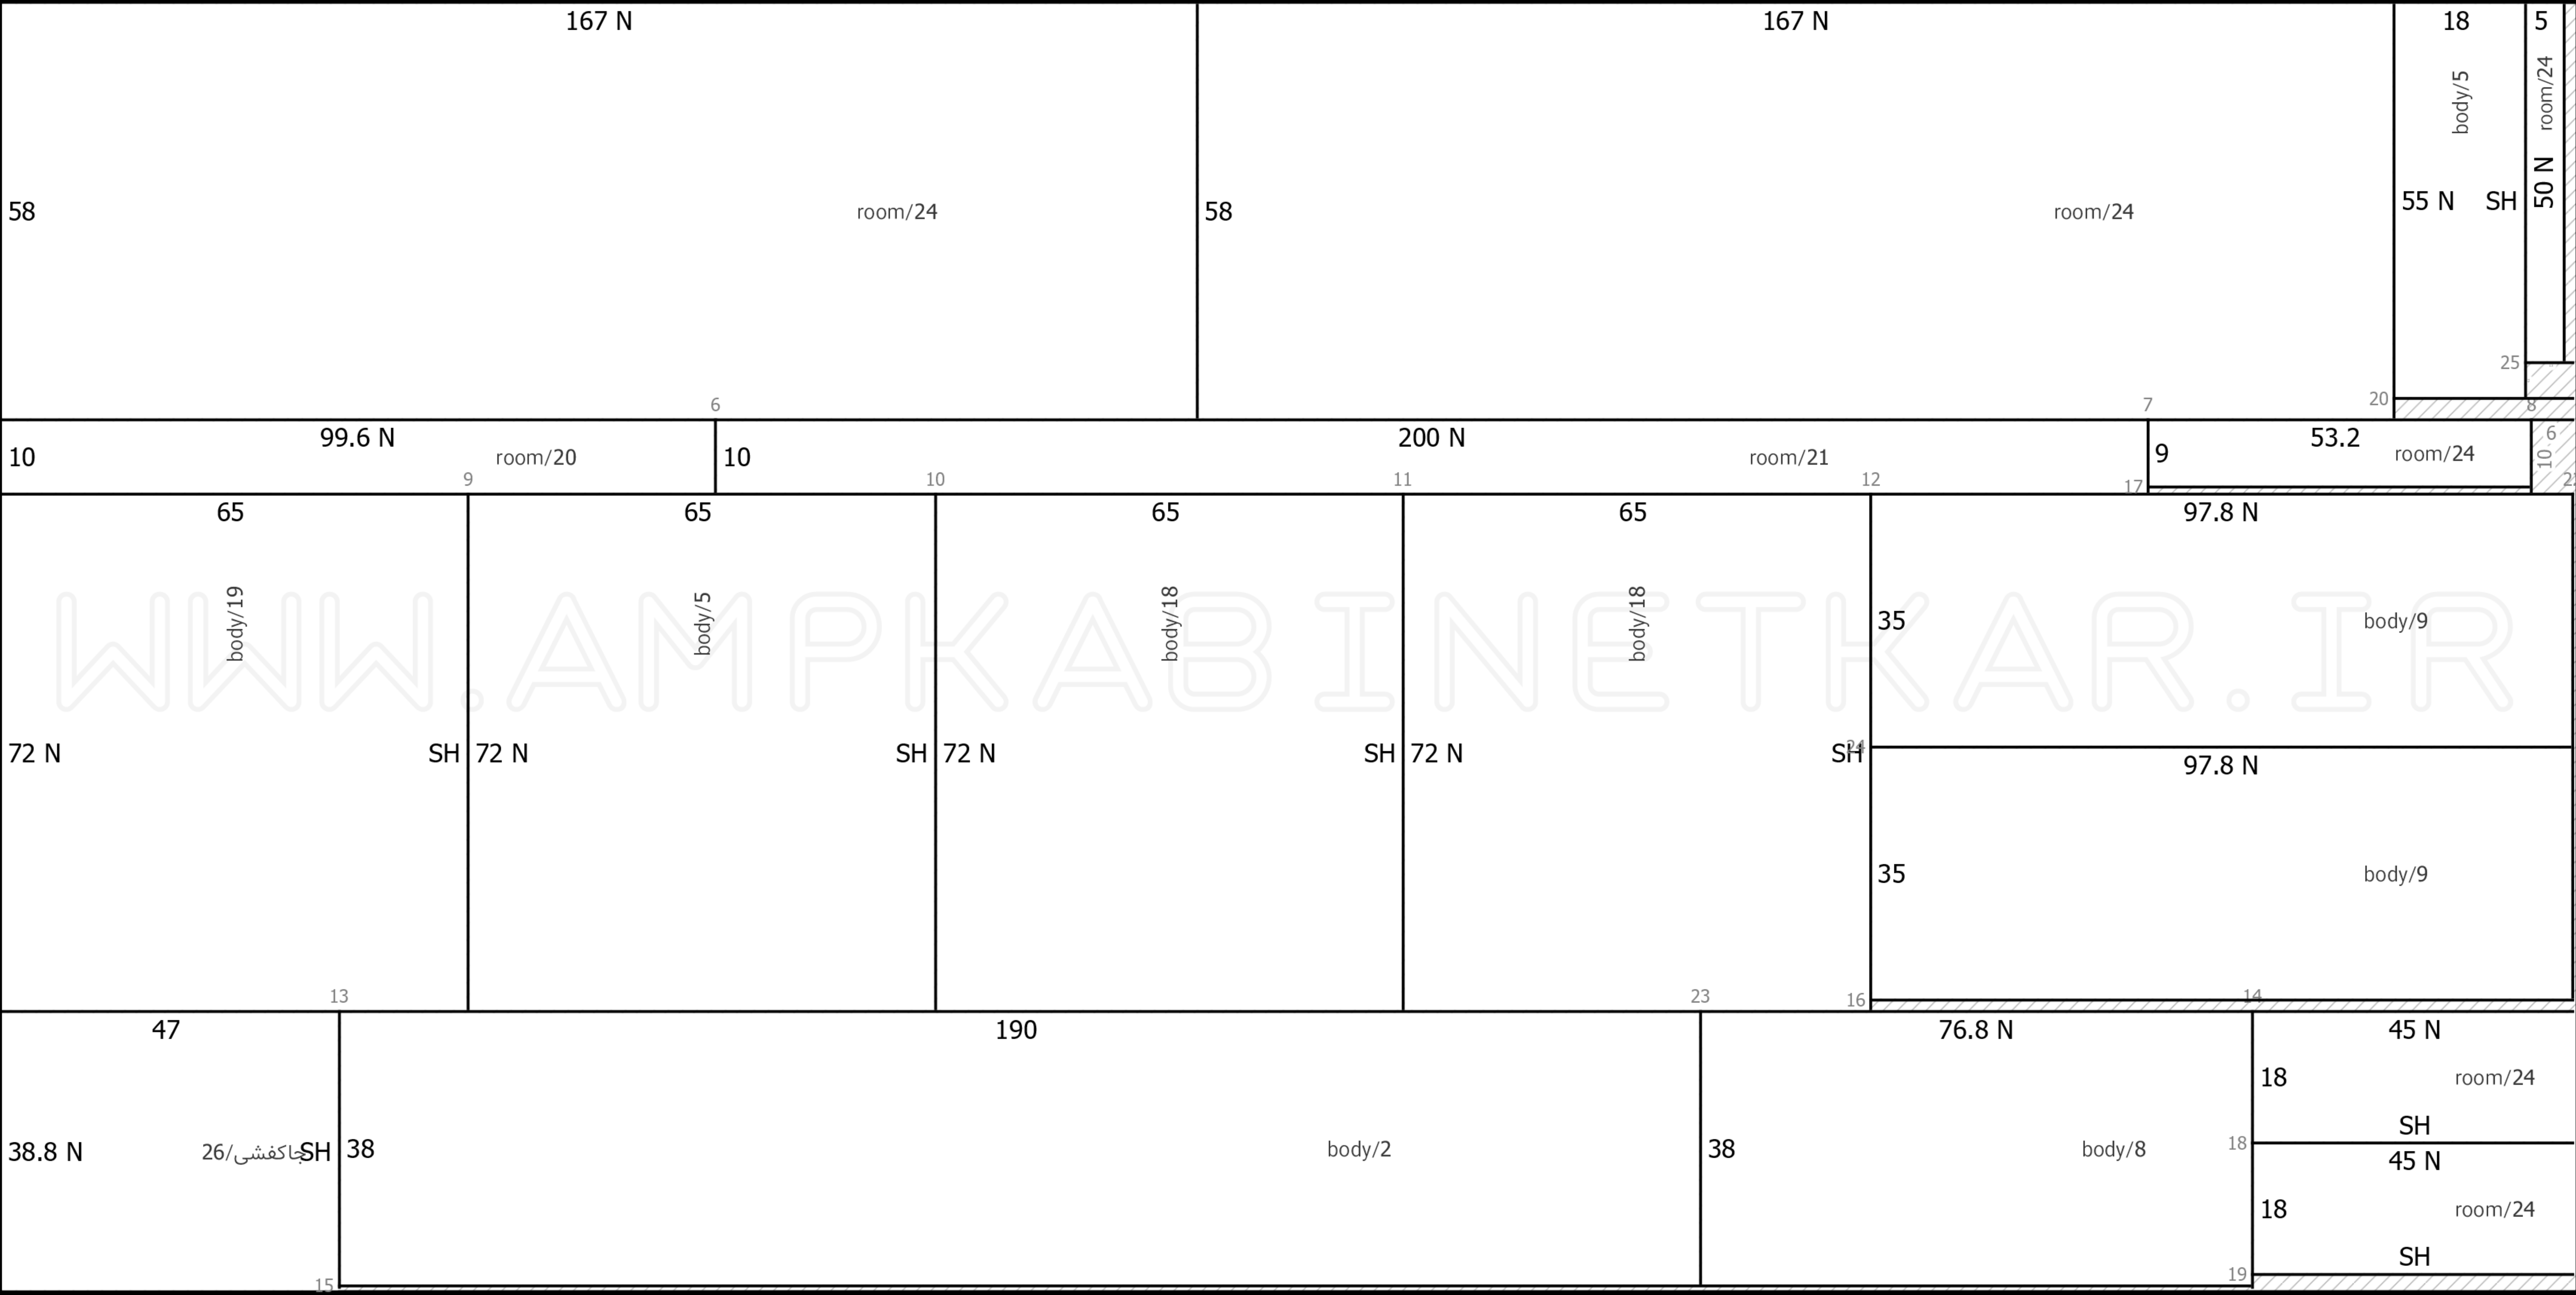

$$362 \times 182 = 1$$

ضخامت های لبه زائد: $\leftarrow 1 \quad \uparrow 1 \quad \Rightarrow 1 \quad \downarrow 1$

آقای بابایی / بدنه / 6

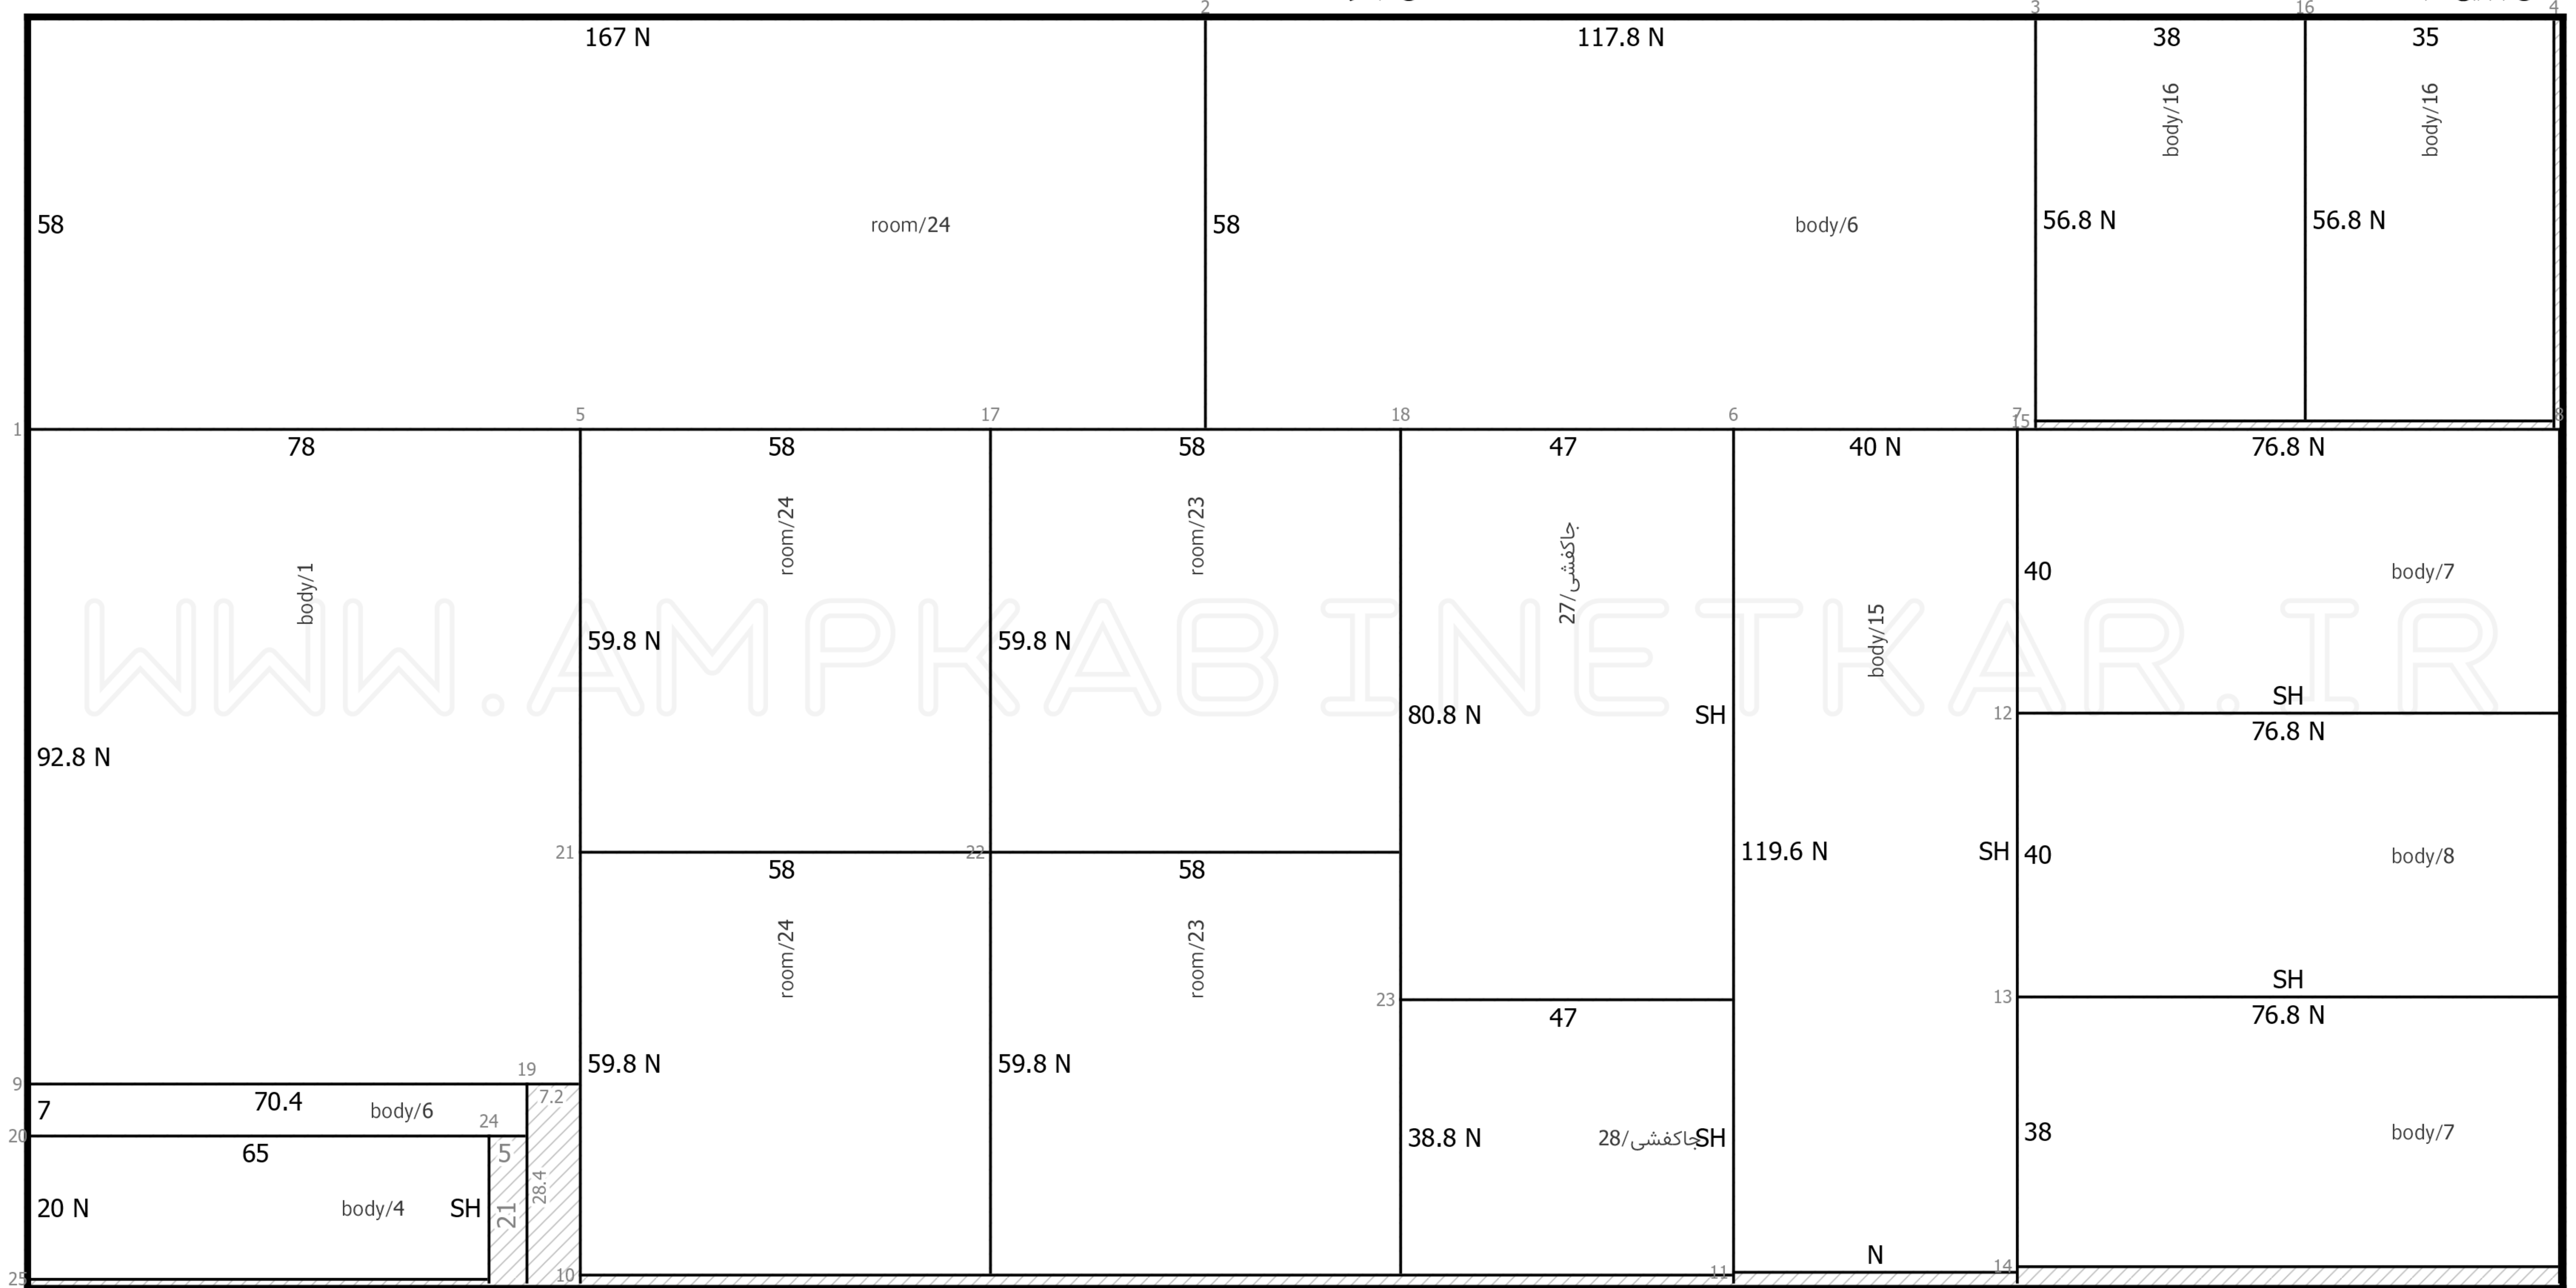


مساحت استفاده شده: 6.3 مترمربع | مساحت باقیمانده: 0.09 مترمربع | تعداد قطعات: 17 | تعداد قطعات اضافه: 8 | تعداد برش: 25 | بهینه سازی: 98.7% | پرتی: 1.3%


362 × 182 = 1

ضخامت های لبه زائد: 1 ↓ 1 ⇒ 1 ↑ 1 ⇐ 1

آقای بابایی / بدنه / 7

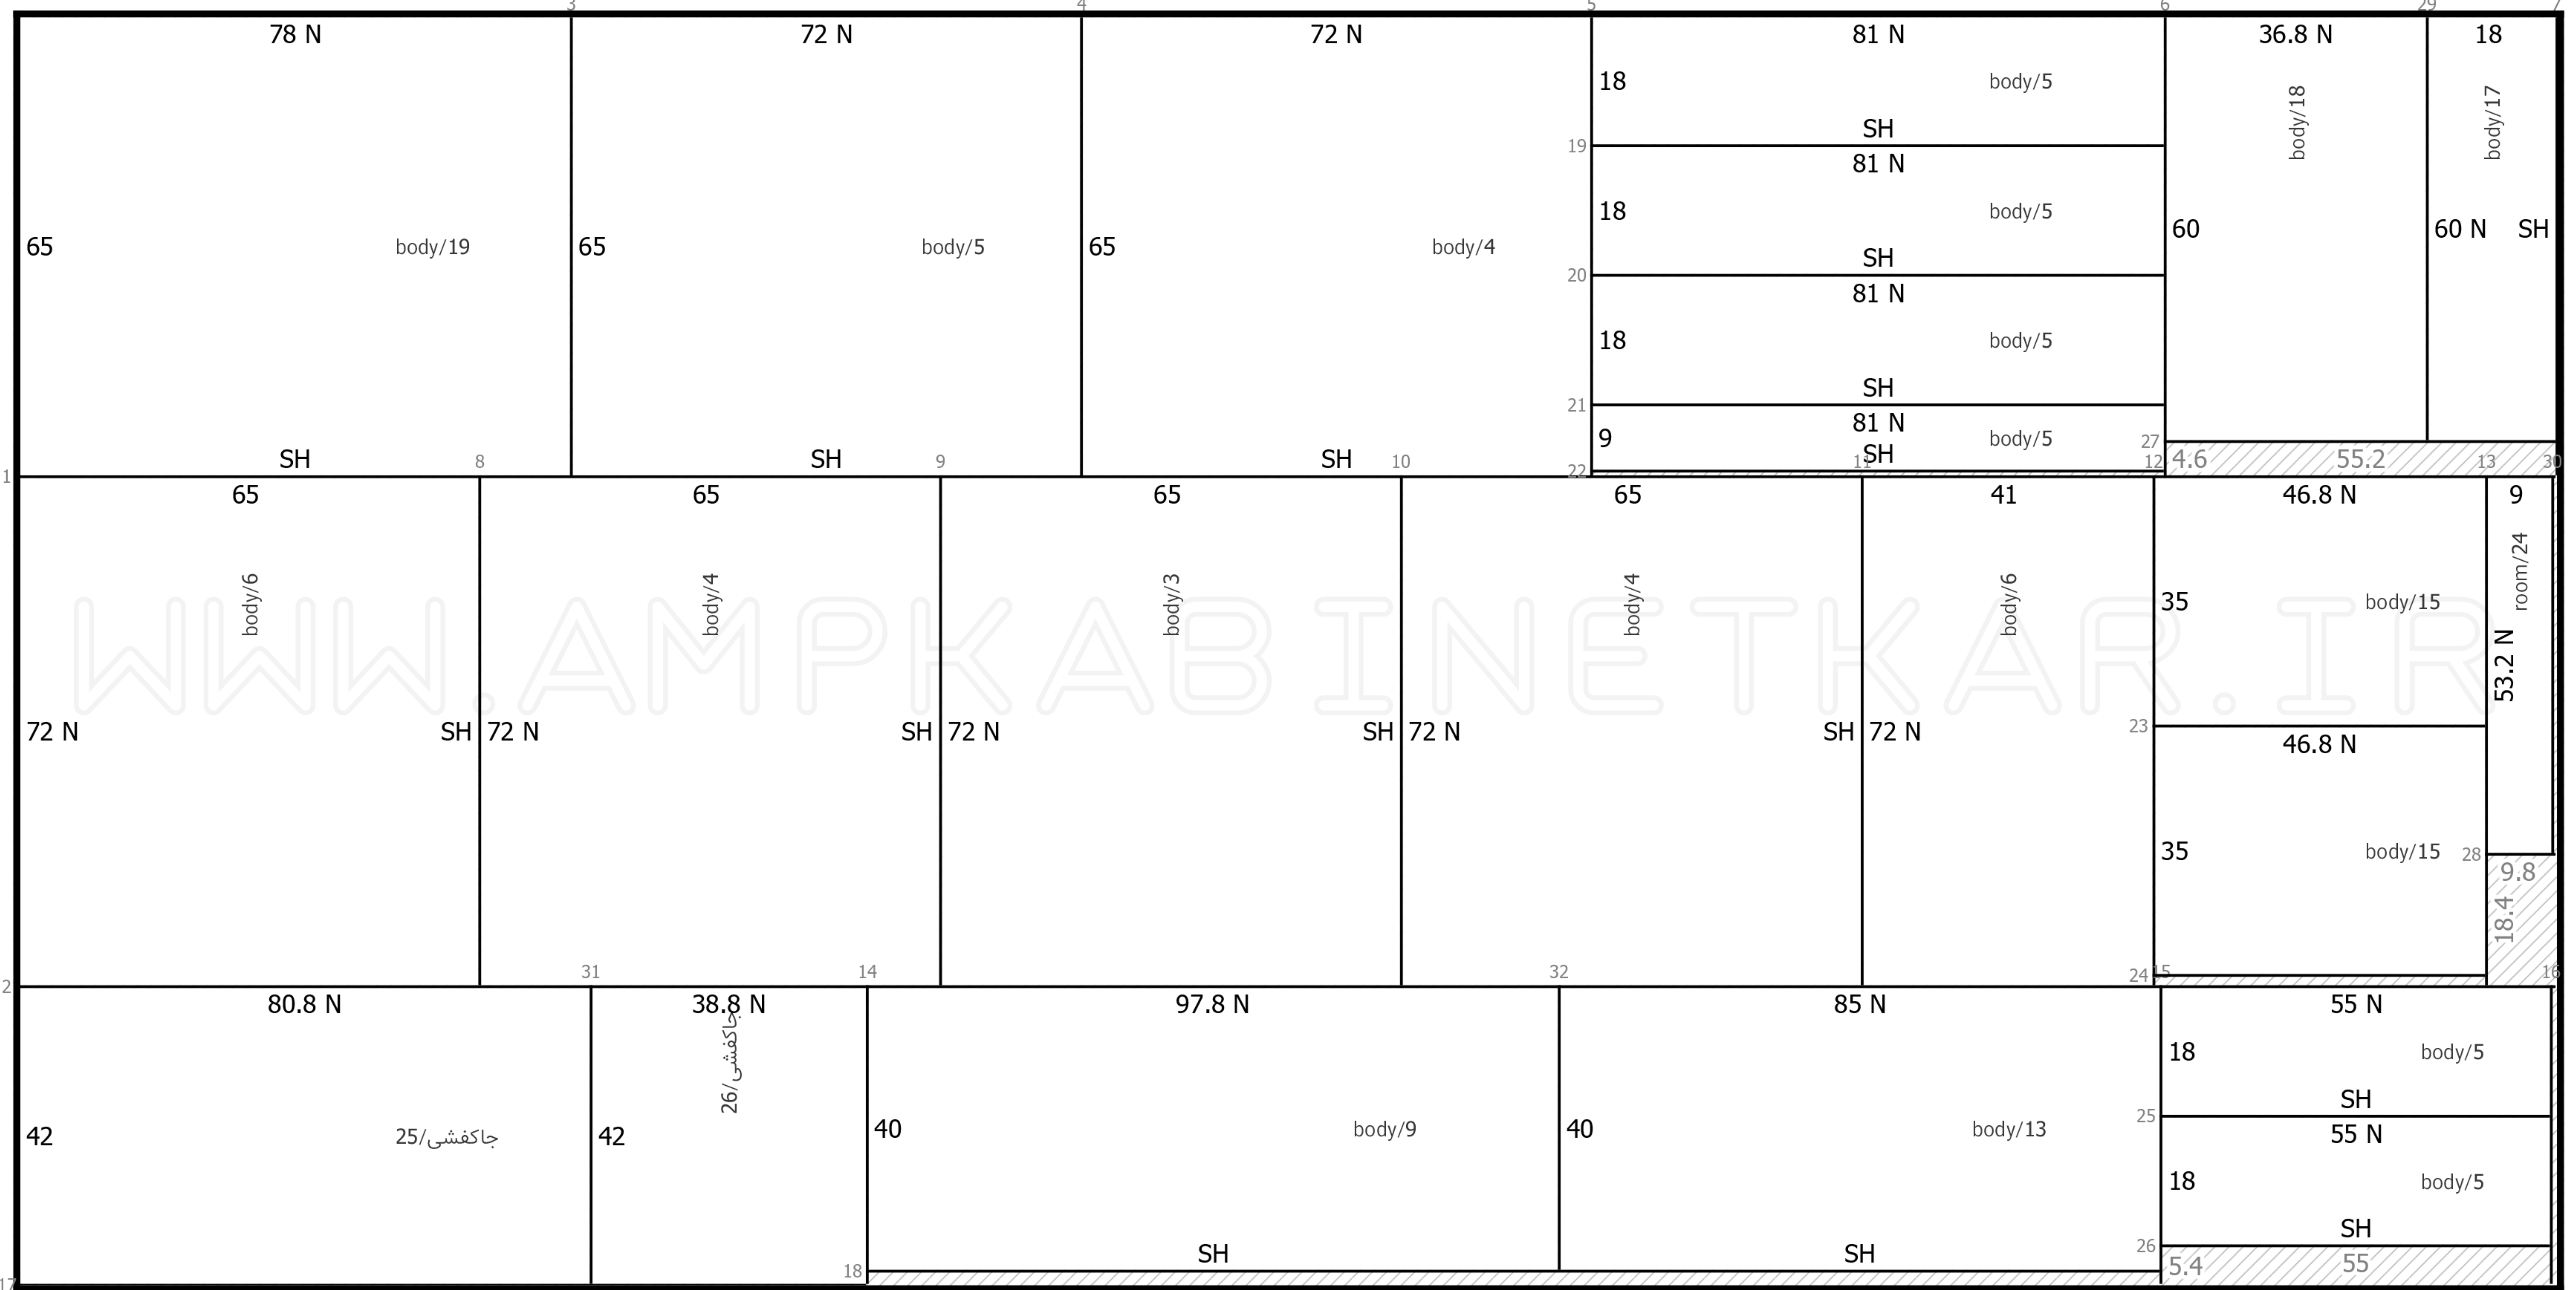


مساحت استفاده شده: 6.26 مترمربع | مساحت باقیمانده: 0.12 مترمربع | تعداد قطعات: 23 | تعداد قطعات اضافه: 8 | تعداد برش: 32 | بهینه سازی: 98.2% | پرتی: 1.8%

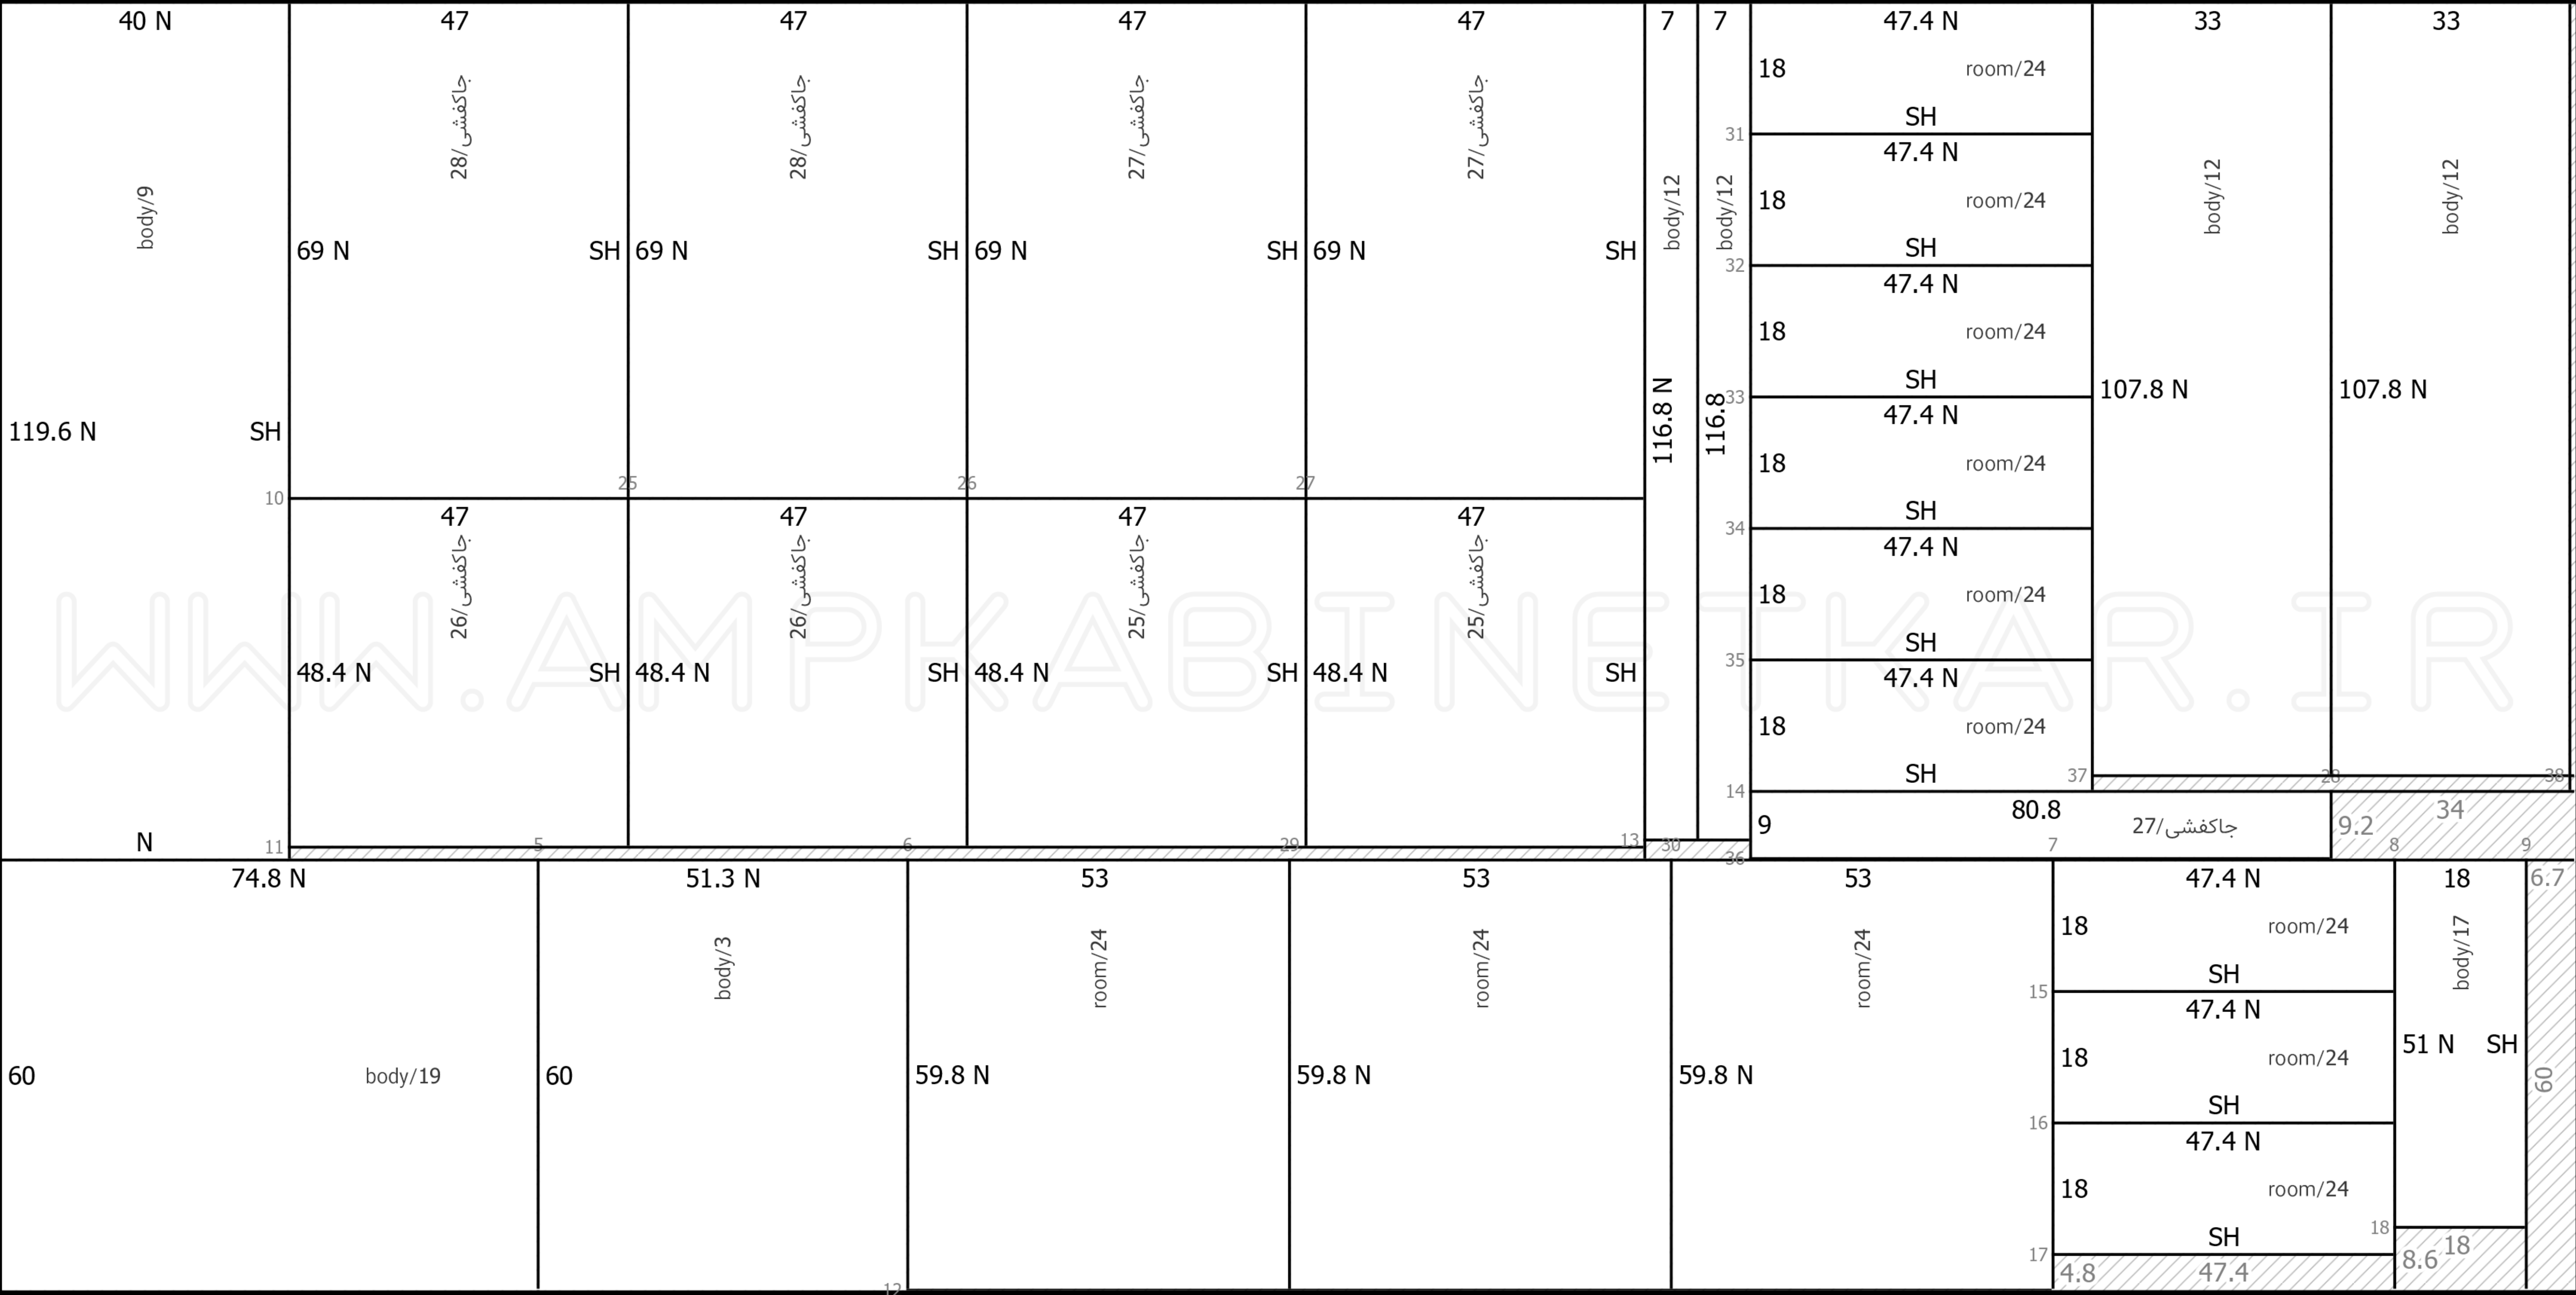

362 × 182 = 1

ضخامت های لبه زائد: 1 ↓ 1 ⇒ 1 ↑ 1 ⇐ 1

آقای بابایی / بدنه / 9

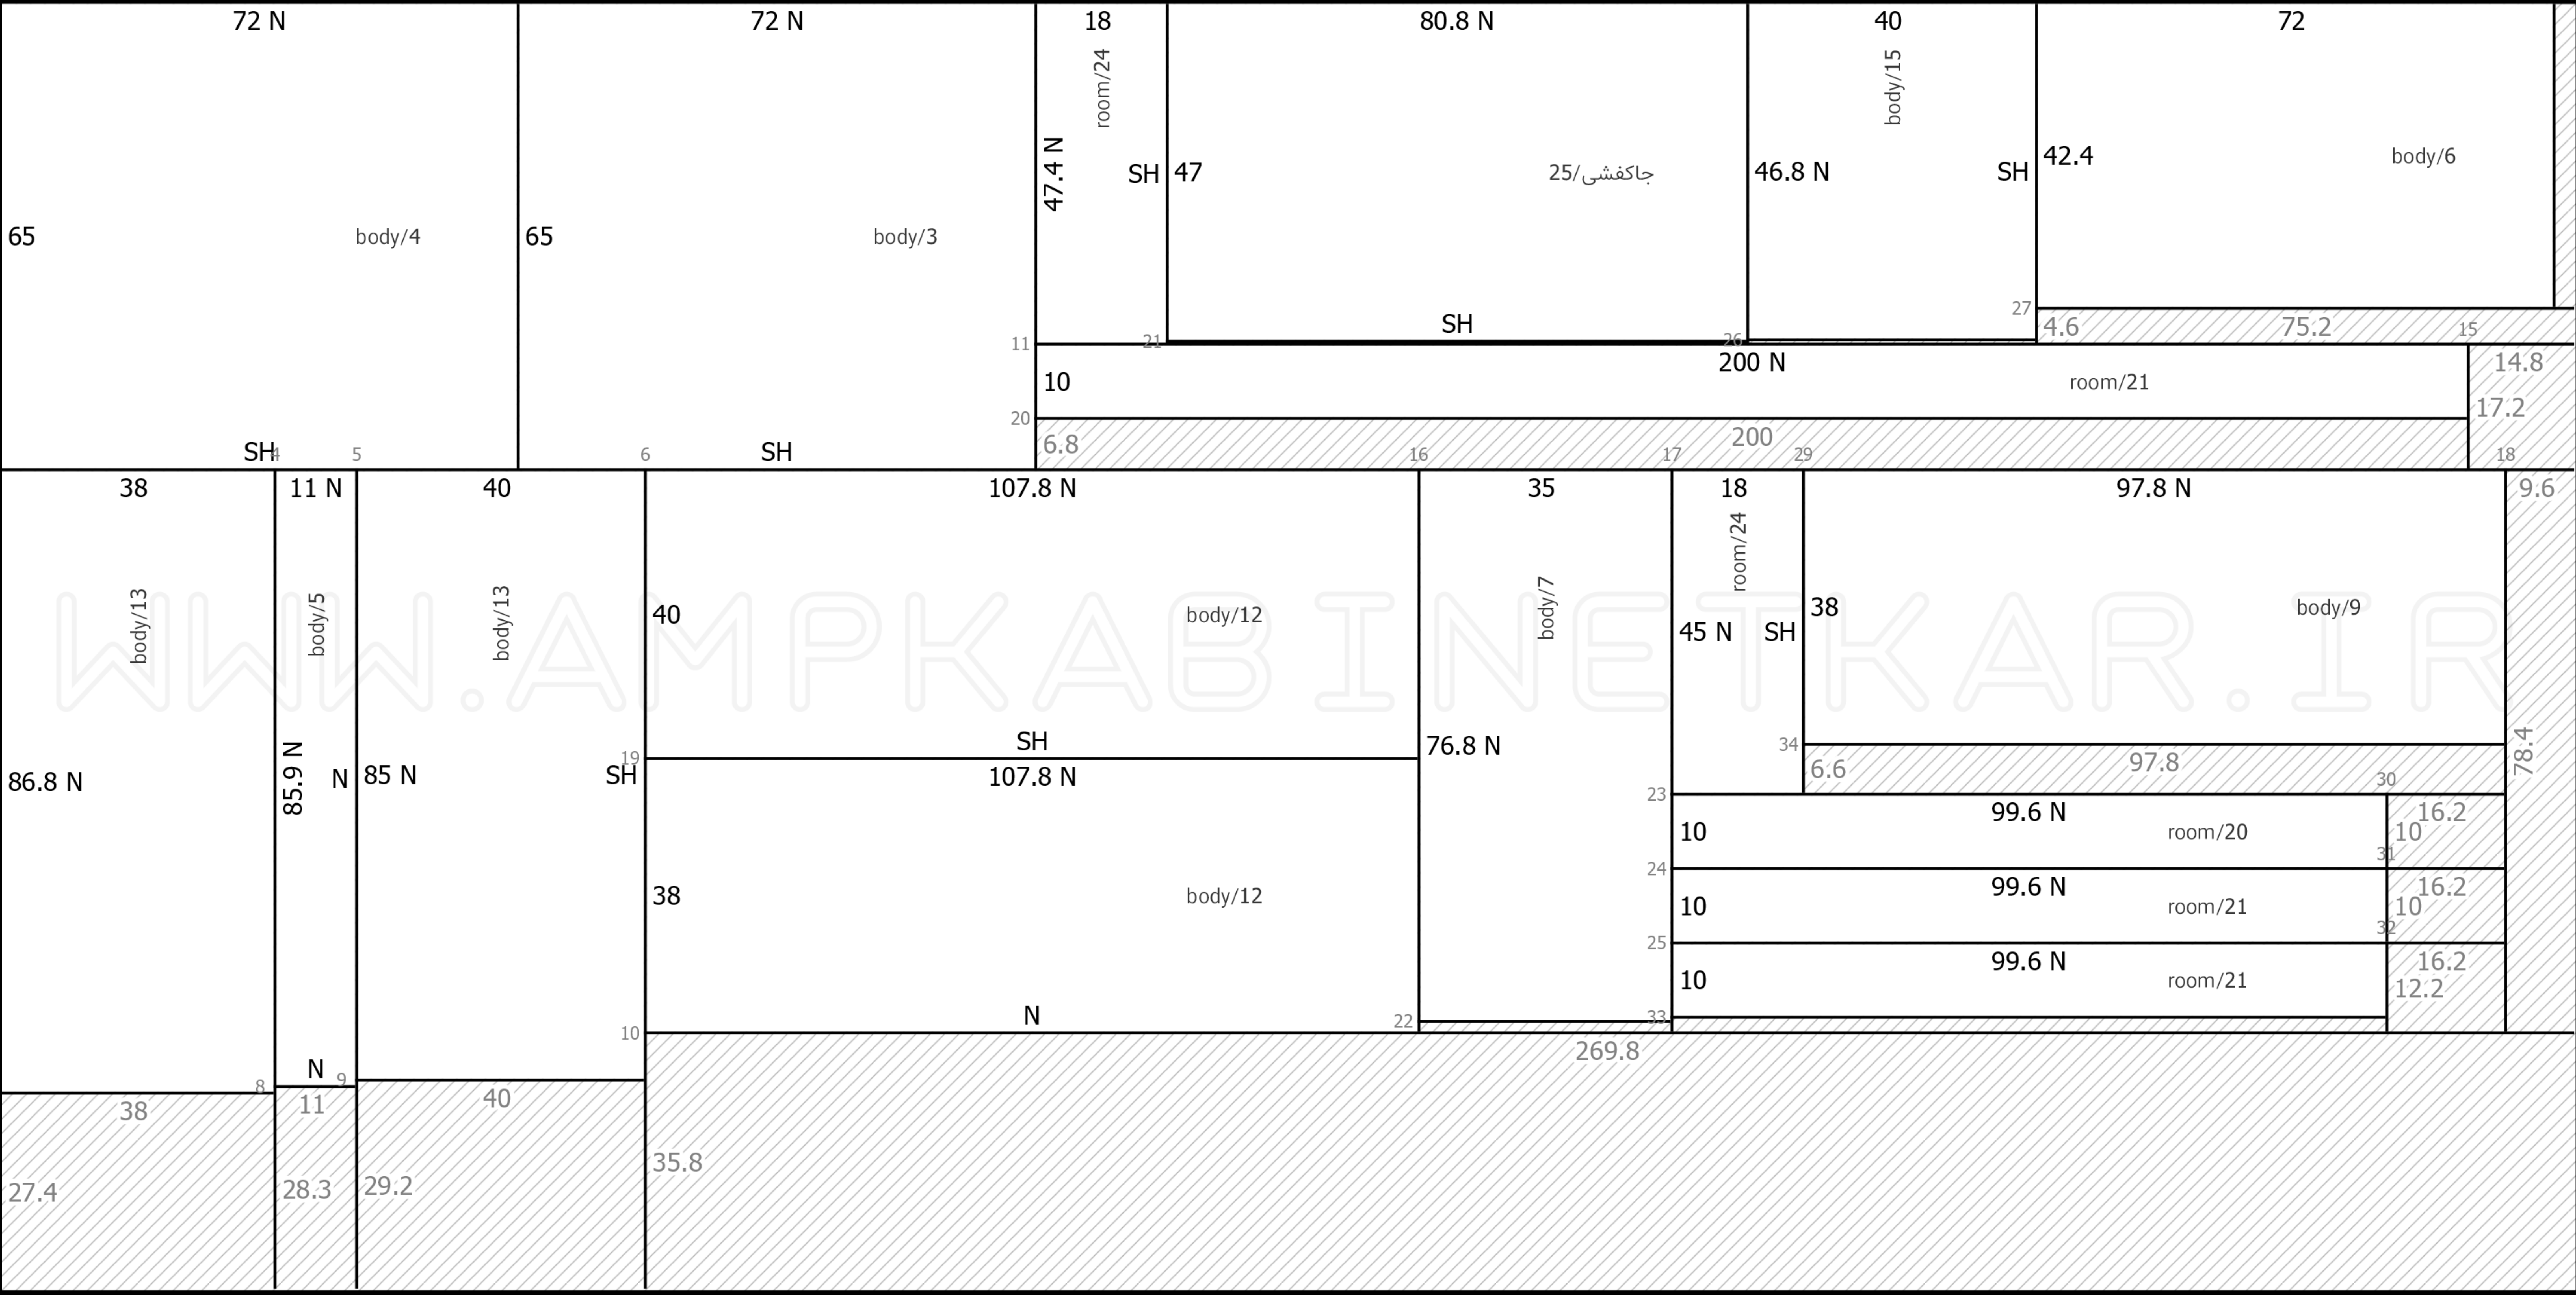

مساحت استفاده شده: 4.72 مترمربع | مساحت باقیمانده: 1.64 مترمربع | تعداد قطعات: 18 | تعداد قطعات اضافه: 16 | تعداد برش: 34 | بهینه سازی: 75.1% | پرتی: 24.9%